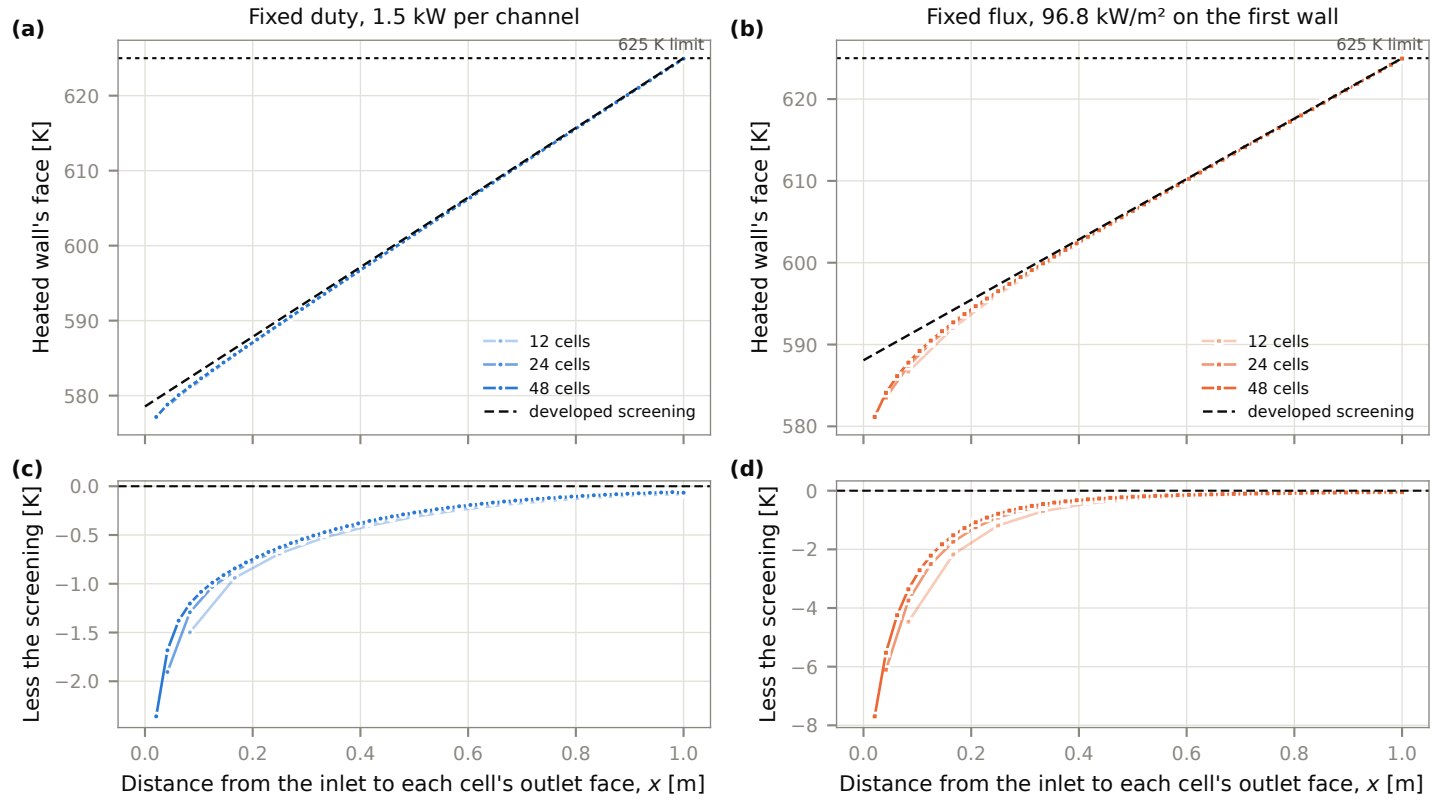
(a)
Fixed duty, 1.5 kW per channel
625 K limit
Heated wall's face [K]
620
610
600
590
580
12 cells
24 cells
48 cells
developed screening
(b)
Fixed flux, 96.8 kW/m² on the first wall
625 K limit
Heated wall's face [K]
620
610
600
590
580
12 cells
24 cells
48 cells
developed screening
(c)
Less the screening [K]
0.0
−0.5
−1.0
−1.5
−2.0
0.0
0.2
0.4
0.6
0.8
1.0
Distance from the inlet to each cell's outlet face, x [m]
(d)
Less the screening [K]
0
−2
−4
−6
−8
0.0
0.2
0.4
0.6
0.8
1.0
Distance from the inlet to each cell's outlet face, x [m]