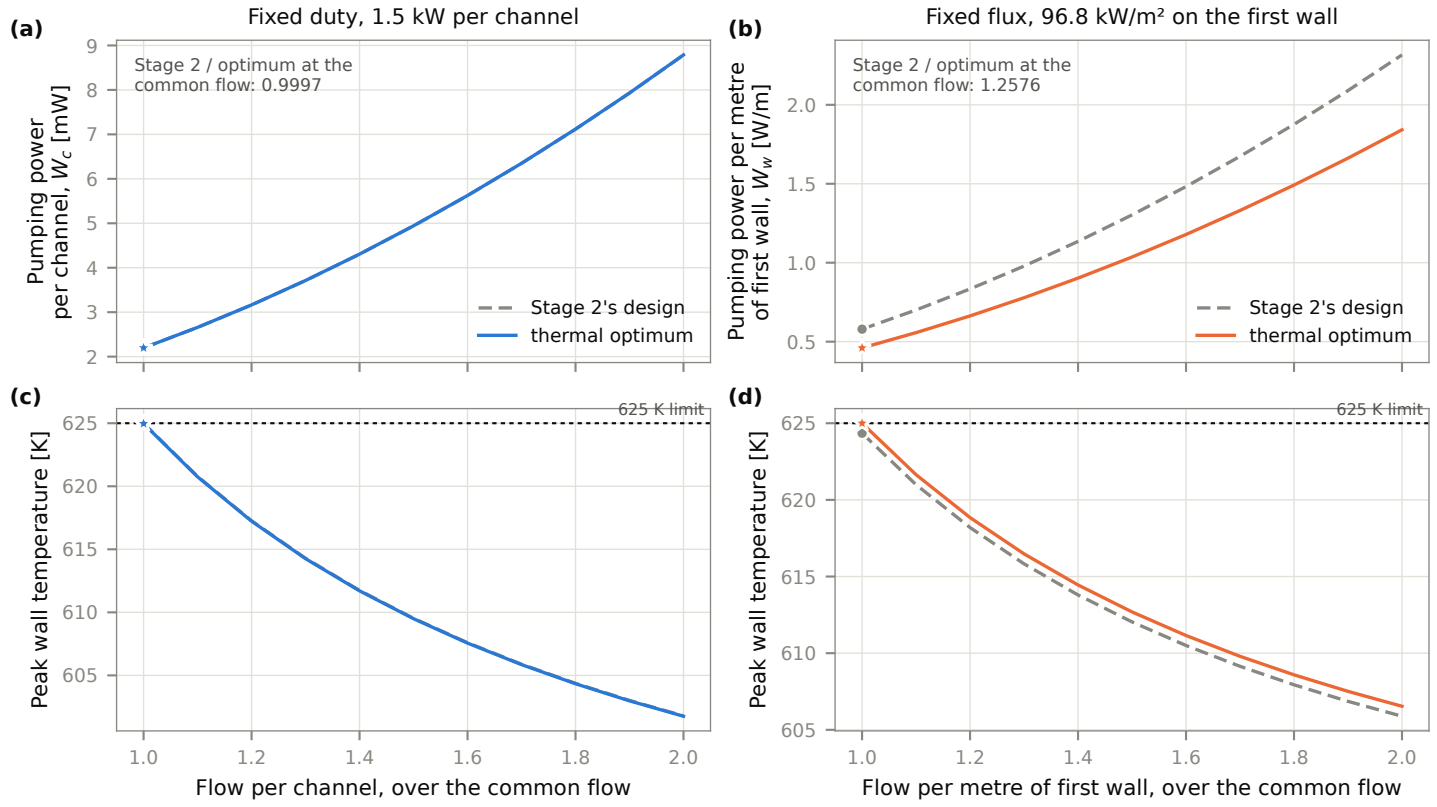
(a)
Fixed duty, 1.5 kW per channel
Stage 2 / optimum at the common flow: 0.9997
Pumping power per channel, W_c [mW]
Stage 2's design
thermal optimum
(b)
Fixed flux, 96.8 kW/m² on the first wall
Stage 2 / optimum at the common flow: 1.2576
Pumping power per metre of first wall, W_w [W/m]
Stage 2's design
thermal optimum
(c)
625 K limit
Peak wall temperature [K]
Flow per channel, over the common flow
(d)
625 K limit
Peak wall temperature [K]
Flow per metre of first wall, over the common flow